


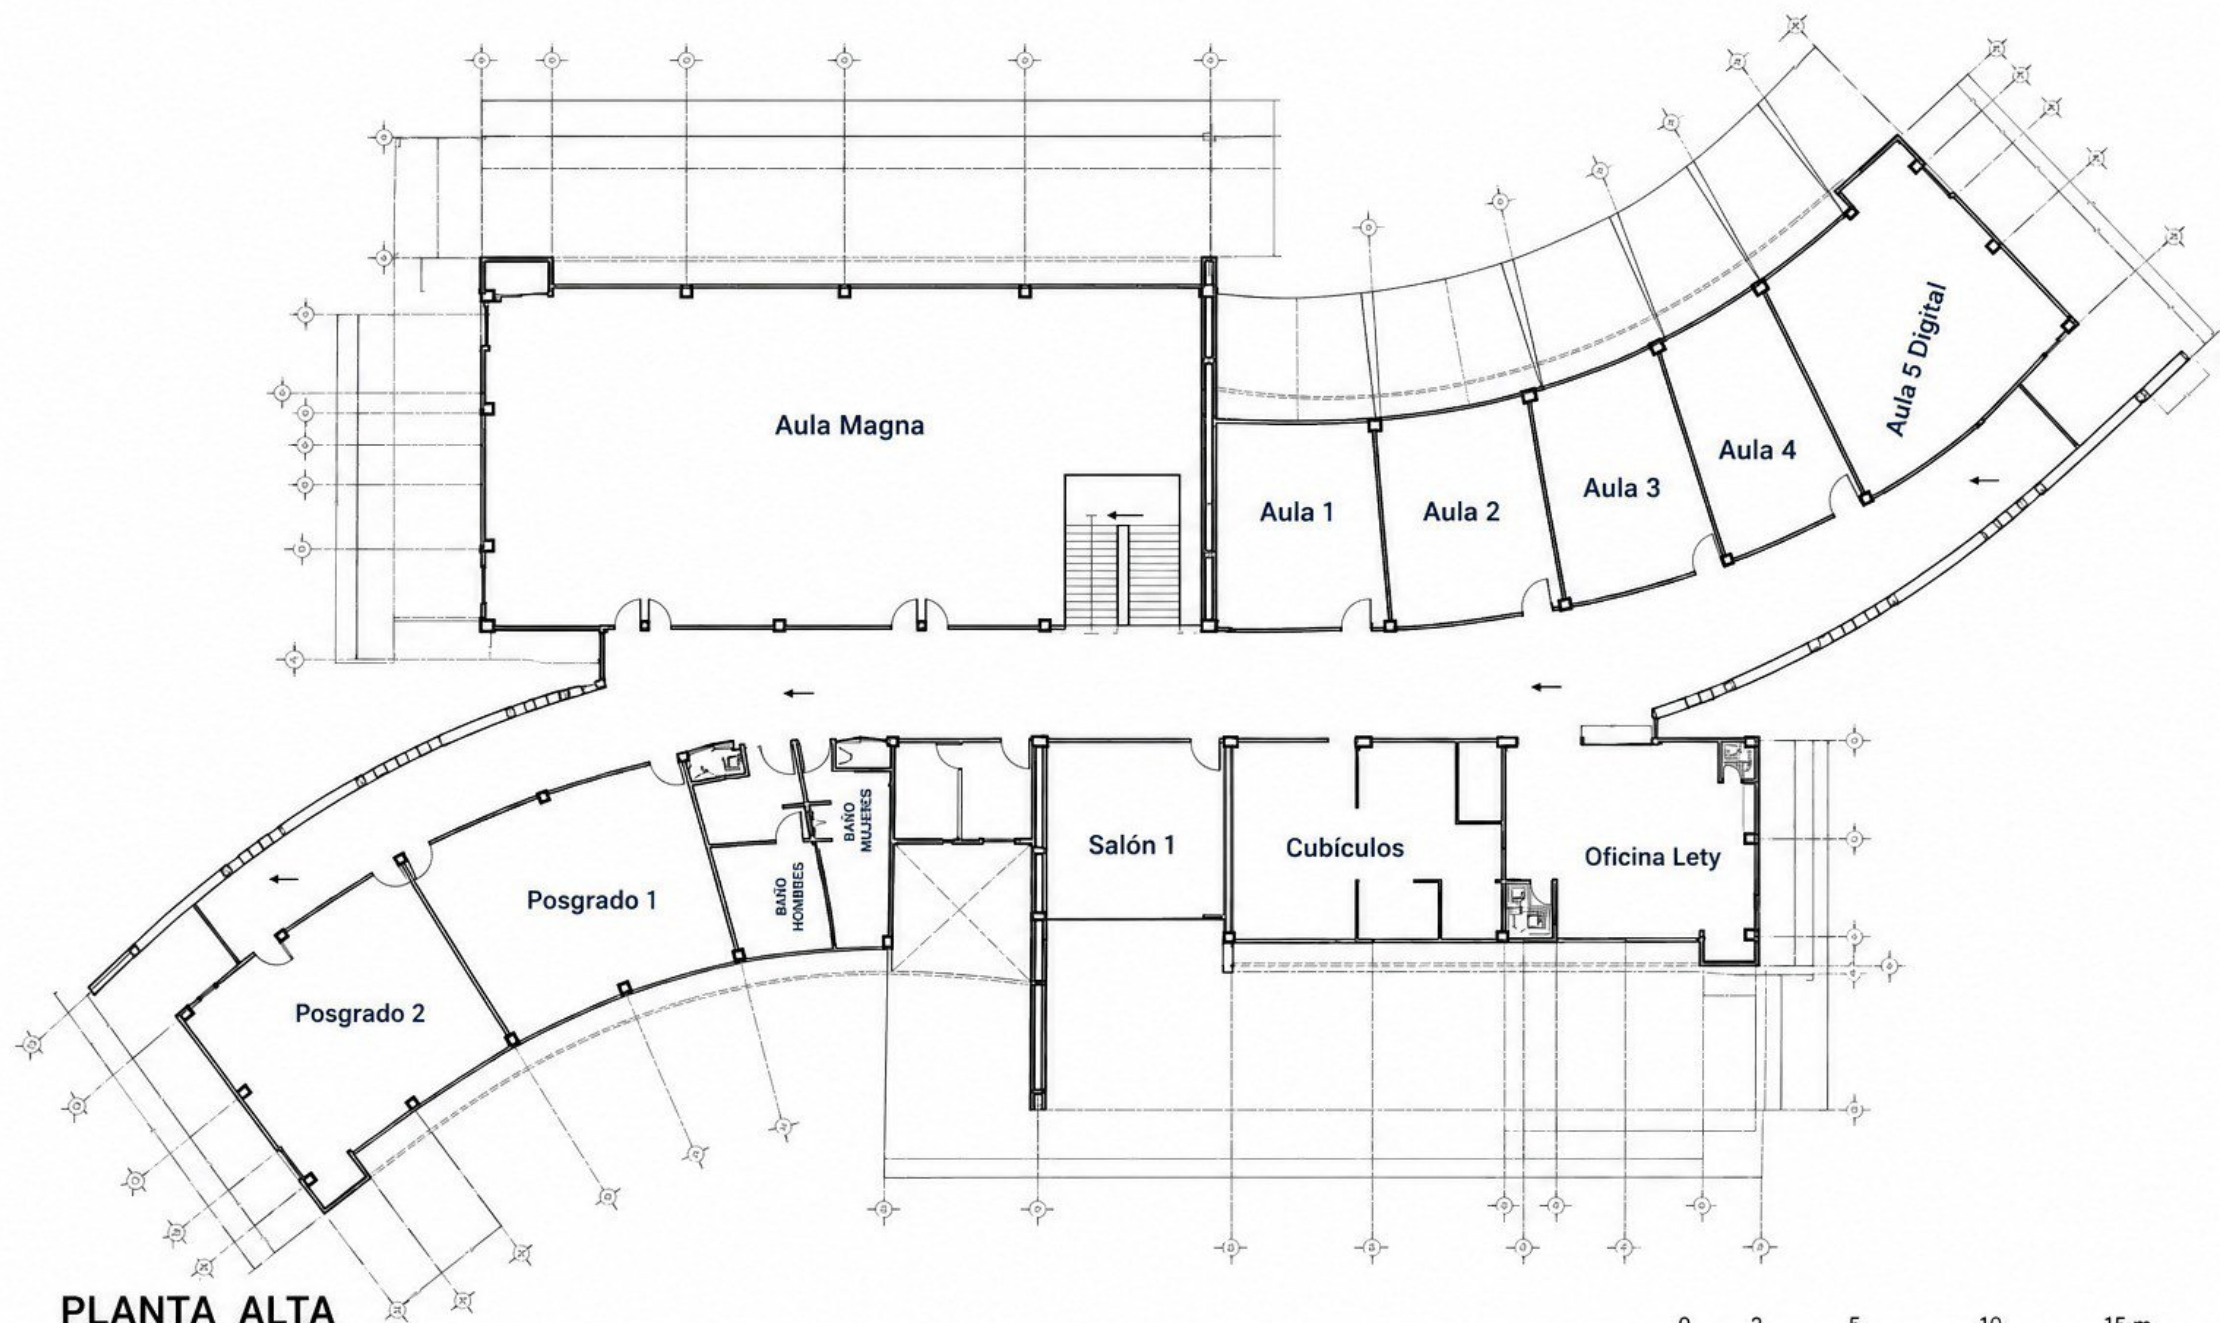

PLANTA ALTA

EDIFICIO PIDET

0 2 5 10 15 m